DAVID VOEGELE
JUDGE-EXECUTIVE
DVOEGELE@OLDHAMCOUNTYKY.GOV

KEVIN NUSS
DEPUTY JUDGE-EXECUTIVE
KNUSS@OLDHAMCOUNTYKY.GOV

RYAN FISCHER
DIRECTOR
RFISCHER@OLDHAMCOUNTYKY.GOV

OLDHAM COUNTY
PLANNING & DEVELOPMENT SERVICES
100 WEST JEFFERSON STREET, SUITE 3, LAGRANGE, KENTUCKY 40031
OFFICE 502-222-1476 • FAX 502-222-3213
WWW.OLDHAMCOUNTYKY.GOV

Staff Packet

Zoning Map Amendment
3000 Block of Commerce Parkway, La Grange, Parcel No. 39-00-00-2A

The following documents are the Staff Packet for the Zoning Map Amendment for 3000 Block of Commerce Parkway La Grange, Parcel No. 39-00-00-2A. This includes:

1. Ordinance
2. Letter to Judge Voegele
3. County Attorney Review Form
4. Staff Report
5. Application
6. Plan
7. Planning Commission Minutes
8. TRC Minutes
9. Community Meeting Minutes

COMMONWEALTH OF KENTUCKY
OLDHAM COUNTY
ORDINANCE NO. KOC 26-920-045

AN ORDINANCE RELATING TO A CHANGE IN THE OLDHAM COUNTY ZONING MAP REZONING TWO TRACTS OF LAND TOTALING 66.8 ACRES OF LAND LOCATED AT THE 3000 BLOCK OF COMMERCE PARKWAY, LA GRANGE, KENTUCKY (PARCEL NUMBER 39-00-00-2A) FROM THE EXISTING PUD, PLANNED UNIT DEVELOPMENT DISTRICT TO I-1, LIGHT INDUSTRIAL DISTRICT ZONING CLASSIFICATION.

* * * * *

WHEREAS, the Oldham County Planning & Zoning Commission on application of Glenview Partners Acquisitions, LLC desires to change the Oldham County zoning map in reference to two tracts of land totaling 66.8 acres located at the 3000 block of Commerce Parkway, La Grange, Kentucky (Parcel Number 39-00-00-2A) and seeks a zoning map change for the 66.8 acres from the existing PUD, Planned Unit Development District to I-1, Light Industrial District zoning classification; and,

WHEREAS, the Oldham County Planning & Zoning Commission did advertise and conduct a public hearing on the issue of rezoning the hereinafter described 66.8 acres on September 22, 2026 (Docket PZ-26-024), and at the conclusion of said hearing, did find that the map amendment is in agreement with the Comprehensive Plan and recommended to the Oldham County Fiscal Court that said zoning classification on the hereinafter described 66.8 acres be changed as requested; and,

WHEREAS, the Oldham Fiscal Court did advertise and conduct a public hearing on the recommended zoning map change, and Fiscal Court having made the necessary findings and conclusions justifying said zoning map change and said

Fiscal Court having voted to adopt the zoning map change at its regular meeting conducted November 17, 2026.

NOW, THEREFORE, BE IT ORDAINED BY THE FISCAL COURT OF OLDHAM COUNTY, COMMONWEALTH OF KENTUCKY, THAT:

The Oldham County zoning map controlling the zoning classification of the hereinafter described 66.8 acres from the existing PUD, Planned Unit Development District to I-1, Light Industrial District classification located at the 3000 block of Commerce Parkway, La Grange, Kentucky (Parcel Number 39-00-00-2A). This zoning map change is accompanied by and contingent upon any and all binding elements to be recorded as restrictions on the land and its usage with the Oldham County Court Clerk at La Grange, Kentucky.

TRACT NO. 1:

COMMENCING at a set 1/2" by 18" iron pin with cap stamped "McCloud 4505" in the northwest right-of-way line of Commerce Parkway, said iron pin being the most northerly corner of Tract A, as shown and described in that certain Agreement for Dedication of Public Right-Of-Way, of record in Deed Book 612, Page 111 in the Office of the Clerk of Oldham County, Kentucky, and said iron pin being the southernmost corner of a property conveyed to Smith Capital Partners, LLC, of record in Deed Book 1377, Page 456 in the Clerk’s Office aforesaid; thence running with the western lines of said Smith Capital Partners, LLC the following three courses: N19°22'15"W, 7.92' to a point; N35°06'15"W, 212.00' to a point; N16°06'15"W, 667.07' to a point, the True Point of BEGINNING; thence S69°49'08"W, 1126.43' to a point; thence N19°24'38"W, 873.82' to a point in the southeast right-of-way line of CSX Railroad; thence with said railroad right-of-way line N62°52'39"E, 1012.75' to a point; thence S24°51'29"E,313.64' to a point; thence S41°08'17"E, 64.94' to a point; thence N72°26'13"E, 104.71' to a point; thence S16°06'15"E, 619.68’ to the True Point of BEGINNING, containing 23.71 acres.

TRACT NO. 2:

BEGINNING at a set 1/2" by 18" iron pin with cap stamped "McCloud 4505" in the northwest right-of-way line of Commerce Parkway, said iron pin being the most northerly corner of Tract A, as shown and described in that certain Agreement for Dedication of Public Right-Of-Way, of record in Deed Book 612, Page 111 in the Office of the Clerk of Oldham County, Kentucky, and said iron pin being the southernmost corner of a property conveyed to Smith Capital Partners, LLC, of record in Deed Book 1377, Page 456 in the Clerk's Office aforesaid; thence with said northwest right-of-way line the following two courses: S55°53'15"W, 1436.78' to a point; thence with the arc of a curve to the right having a radius of 768.51' and a chord bearing and distance of S71°00'40"W, 401.02' to a point; thence N15°32'53"W, 1219.71' to a point; thence N69°49'08"E, 563.44' to a point; thence N69°49'08"E, 1126.43' to a point; thence S16°06'15"E, 667.07' to a point; thence S35°06'15"E, 212.00' to a point; thence S19°22'15"E, 7.92' to the Point of BEGINNING, containing 43.07 acres.

Dated this _____ day of _____, 2026.

_____

DAVID VOEGELE
Oldham County Judge/Executive

ATTEST:

_____
Oldham County Fiscal Court Clerk

DAVID VOEGELE
JUDGE-EXECUTIVE
DVOEGELE@OLDHAMCOUNTYKY.GOV

KEVIN NUSS
DEPUTY JUDGE-EXECUTIVE
KNUSS@OLDHAMCOUNTYKY.GOV

RYAN FISCHER
DIRECTOR
RFISCHER@OLDHAMCOUNTYKY.GOV

OLDHAM COUNTY
PLANNING & DEVELOPMENT SERVICES
100 WEST JEFFERSON STREET, SUITE 3, LAGRANGE, KENTUCKY 40031
OFFICE 502-222-1476 • FAX 502-222-3213
WWW.OLDHAMCOUNTYKY.GOV

Date: October 21, 2026

TO: David Voegele, Judge-Executive
100 W Jefferson Street
LaGrange, KY 40031

RE: Ordinance No. KOC-26-920-045
Glenview Partners Acquisitions LLC
3000 Block of Commerce Parkway La Grange, Parcel No. 39-00-00-2A
Zoning Map Amendment

Dear Judge Voegele,

In an effort to make sure items are heard by the legislative bodies in a timely manner, we are sending you notice of this approved docket item.

On September 22, 2026, the Oldham County Planning and Zoning Commission held a public hearing for a request for a Zoning Map Amendment for the above referenced property. The motion to approve the Zoning Map Amendment carried. The minutes will be approved at the Planning Commission meeting on October 27, 2026, and will be sent following approval.

Please tentatively place this item on the docket for the first reading on ***November 3, 2026*** and for the second reading/public hearing on ***November 17, 2026***. The legal description of the proposed zoning map amendment is enclosed.

Thank you for your assistance and please advise us as to other information needed.

Sincerely,

Cayley Crum

Cayley Crum
Planner I
Oldham County Planning and Development

Cc: Oldham County Fiscal Court Clerk

David Voegele
Judge Executive
dvoegele@oldhamcountyky.gov

Kevin Nuss
Deputy Judge Executive
knuss@oldhamcountyky.gov

FISCAL COURT AGENDA ITEM REQUEST
&
COUNTY ATTORNEY REVIEW FORM

October 15, 2026
Today's Date

KOC-26-920-045 Zoning Map Amendment 3000 Block of Commerce Parkway La Grange, Parcel No. 39-00-00-2A
Name of Document and/or Agenda Item

Ryan Fischer, Planning & Development – rfischer@oldhamcountyky.gov / 502-222-1476
Submitted by (Name – Department - Committee) (phone / email)

Does this require Fiscal Court's approval? __X__ yes ____ no

November 17, 2026
Fiscal Court Presentation Date

Who will be presenting Item to Fiscal Court? Cayley Crum, Planning & Development
(Ex: Committee, Chairperson, Department, Staff, Name)

What action (motion) are you requesting of the court?
Zoning Map Amendment: First Reading – November 3, 2026; Second Reading – November 17, 2026

***** REVIEWED AND APPROVED AS TO FORM & LEGALITY BY COUNTY ATTORNEY *****

D Berry Baxter
(Signature)


10-21-2026
Date

D. Berry Baxter, Oldham County Attorney

OLDHAM COUNTY
Fiscal Court
November 17, 2026

Summary of Application:

Ordinance:	**KOC 26-920-045**
Request:	**Zoning Map Amendment**
Applicant:	Glenview Partners Acquisitions, LLC
Location:	3000 block of Commerce Parkway, La Grange
Existing Land Use:	Undeveloped
Existing Zoning:	PUD, Planned Unit Development District
Proposed Zoning	I-1, Light Industrial District
Total Site Size:	66.8-acres
Tax Parcel:	39-00-00-2A

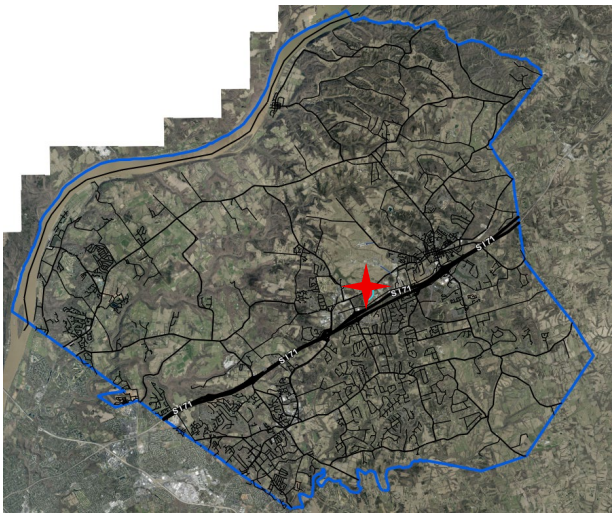

Surrounding Zoning:

North – Land Use: Institutional
Zoning: AG-1

South – Land Use: Undeveloped/ Residential
Zoning: CO-1, R-4

West – Land Use: Undeveloped
Zoning: PUD

East – Land Use: Industrial
Zoning: IPD

Fiscal Court Action:

Ordinance No. KOC 26-920-045 – An application has been filed by Glenview Partners Acquisitions, LLC for a Zoning Map Amendment on property located at the 3000 block of Commerce Pkwy, La Grange. The property is 66.8-acres and currently zoned PUD, Planned Unit Development District with a proposed zoning of I-1, Light Industrial District.

Case History:

Pre-Application Meeting: 7/20/2026
Neighborhood Meeting: 7/16/2026
Technical Review Committee: 8/19/2026
Adjoining Property Owner Notices Mailed: 10/21/2026
Public Notice Appeared in the Oldham Era: 10/29/2026
Sign Posted on Property: 10/23/2026
Planning Commission Recommended Approval: 9/22/2026

Site History:
On September 1, 1998, the Oldham County Planning and Zoning Commission recommended approval of a Zoning Map Amendment from I-2, Heavy Industrial District to IPD, Industrial Park District (Docket 2863). The motion carried.

On July 28, 1998, Oldham County Fiscal Court approved a Zoning Map Amendment application from I-2, Heavy Industrial District to IPD, Industrial Park District (Ordinance No. 98-920-128). The motion carried.

On January 24, 2006, Oldham County Planning and Zoning Commission recommended approval a Zoning Map Amendment and approved a Master Plan to be known as Bucker Crossings (PZ-06-004). The requested zoning map amendment was from IPD, Industrial Park District to PUD, Planned Unit Development District. Both motions carried.

On March 21, 2006, Oldham County Fiscal Court approved a Zoning Map Amendment from IPD, Industrial Park District to PUD, Planned Unit Development District (Ordinance No. 06-930-369). The motion carried.

On June 27, 2006, Oldham County Planning and Zoning Commission approved a Development Plan with Conditions of Approval (PZ-06-001). The motion carried.

On September 22, 2026, Oldham County Planning and Zoning Commission recommended approval of a Zoning Map Amendment from PUD, Planned Unit Development District to I-1, Light Industrial District, to Fiscal Court along with the approval of the Development Plan (PZ-26-024). The motion carried.

Conformance with Comprehensive Plan:
The Oldham County Future Land Use Map (2025) predicts that the tract will be Mixed-Use.

Conformance with Zoning Ordinance:
The proposed plan meets all standards in the Oldham County Zoning Ordinance.

Agency Comments:
See TRC comments in the staff packet.

Notes:

1. The applicant is seeking a Zoning Map Amendment from PUD, Planned Unit Development District to I-1, Light Industrial District to facilitate two proposed logistics warehouses.
2. According to Oldham County Comprehensive Zoning Ordinance Section 190-010, the I-1, Light Industrial District is intended to:
    a. Provide commercial use, storage and any manufacturing use, not normally creating a nuisance discernible beyond its property.
3. Rezoning out of the PUD will remove the requirement to comply with the Buckner Crossings Master Plan.
4. The plan proposes two warehouses and four contained offices with a combined 923,200 SF. Tract 1 is 273,400 SF, contains one warehouse, two offices, and 148 parking spaces. Tract 2 is 629,800 SF, contains one warehouse, two offices, and 295 parking spaces.
5. The two warehouses are speculative buildings, and their use is not yet determined.

Motions and Findings:
Every motion to approve a Zoning Map Amendment must state the finding(s) required by statute or regulation and must also state the reasons for the motion. Every motion to deny must state the reasons for the motion. These are procedural due process requirements for all cases before the Commission.

Suggested motions to approve or deny are set out below.

1. **Zoning Map Amendment 3000 block of Commerce Parkway**

Motion to **approve** the zoning map amendment because (any or all of the following):
a. It complies with objectives _____ of the comprehensive plan because _____; and/or
b. The existing zoning classification given to the property is inappropriate and the proposed zoning is appropriate because _____; and/or
c. There have been major changes in the economic, physical or social nature within the area involved which were not anticipated in the adopted Comprehensive Plan and which have substantially altered the basic character of such area. The major changes are _____ and the basic character has changed from _____ to _____.

Motion to **deny** the zoning map amendment because (any or all of the following):
a. It does not comply with the comprehensive plan because _____; and/or
b. The existing zoning classification given to the property is appropriate and the proposed zoning is inappropriate because _____; and/or
c. There have *not* been major changes in the economic, physical or social nature within the area involved, which were not anticipated in the adopted Comprehensive Plan, and which have substantially altered the basic character of such area in that _____.

Proposed Binding Elements:
1. The approval applies only to the plan presented at the November 17, 2026, Oldham County Fiscal Court public hearing.
2. The plan must comply with all established federal, state and county ordinances and requirements and comply with all necessary easement restrictions at the time of construction plan approval.

Sec. 190-030 I-1 Light Industrial District: Permitted Uses

Agricultural Uses

Agricultural Uses

Riding Academies and Stables

Community Facilities

Nursery Schools, Day Nurseries, and

Child Care Centers

Schools, Parks, Playgrounds, Community Centers, and Similar Uses

Commercial

Adult Entertainment Establishments

Art Studios

Colleges and Schools, not for profit (CF)

Funeral Homes and Mortuaries

Household Services

Retail and Personal Service Establishments

Vehicular Repair of any kind

Veterinary Hospitals and Kennels

Vocational Schools

Eating Establishments

Eating Establishments of any kind

Light Industrial

Aircraft Factory or Hangar, not including wind tunnel and testing field

Blacksmith Shop or Horse ShoeingEstablishment

Boat and Marine Supplies

Boat Building

Bottlers, Breweries, Distilleries, and Wineries

Box Factory

Lumber Storage, Millwork, and Sales Mini-Warehouses/Self Storage Facilities

Public Parks and Recreation

Boat Docks and Launching Areas

Recreational Camps, Resorts

Indoor Sports Facilities

Public Parks and Forest Preserves

Public picnic grounds, beaches, bridle and bicycle paths

Religious Institutions

Churches and other Religious Institutions

Utilities

Public Utility Buildings and Facilities

Sec. 190-040 I-1 Light Industrial District: Conditional Uses

Community Facilities and Services

Marinas or Boat Rental

Recreational Vehicle Parks and Campgrounds

Health Services

Hospitals and Institutions

Heavy Industrial

Asphalt Processing

Concrete, Central Mixing and Batching Plant

Fertilizer, Incineration, or Reduction Products

Freight Terminals/Similar Enterprises

Slaughter Houses

Recreation

Amusement Parks, Circus and Carnival Grounds

Aviaries and Zoos

Commercial Rifle, Pistol and Skeet Ranges

(Indoor and Outdoor)

Drive-In Theatres

Private Clubs, country clubs, golf courses except Miniature Courses or Commercial Driving Ranges

Special

Airports, Heliports and Other Airship or Flying Machine Take-off or Landing Facilities

Borrow Pits, Quarry, Gravel Pit, or Stone Mill

Cemeteries, Mausoleums and Crematories

Commercial Lakes

Extraction and Development of Natural Resources

Utilities

Private Utility Buildings and Facilities

Sewage Treatment Plants

Docusign Envelope ID: 4A09B812-4C60-85AF-807A-C46C380A8CE7

Oldham County Planning and Development Services
Application for Legislative Body Review

For Staff Use Only:			
Date: 10/14/26	*Docket No.:*	*Staff:*	*Fee:*
Ordinance #:	*1st Reading:*	*2nd Reading:*	

This application must be submitted in person at the Planning and Development Services Office.

Legislative Body: ☒ Fiscal Court ☐ Crestwood ☐ LaGrange ☐ Pewee Valley

General Information: *(A separate application must be submitted for each individual request.)*

Project Name: Glenview Partners Acquisitions, LLC

Project Address: Hwy 146

Planning Commission Docket Number(s): PZ-26-024

Planning Commission Review Date(s): September 22, 2026

Total Site Acreage: 66.8 Parcel ID 39-00-00-2A

Current Land Use: Vacant Proposed Land Use: Warehouses

Current Zoning: PUD Proposed Zoning: I-1

Proposed Number of Lots/Units:

Signatures:

Owner(s):
Name: Tomato Field LLC Signature: Jackson Woodward

Address: 416 Rolling Lane, Louisville, Kentucky 40207

Phone: Email Address:

Applicant(s): *(if other than owner)*
Name: Glenview Partners Acquisitions, LLC Signature:


Address: 40 S Main Street, Ste 1510, Memphis, TN 38103

Phone: (205) 229-3457 Email Address: todd@glenview-partners.com

Contact: *(if other than owner)*
Name: Clifford Ashburner, Dinsmore & Shohl Signature:


Address: 101 S. Fifth Street #2500, Louisville, KY 40202

Phone: 502-540-2300 Email Address: clifford.ashburner@dinsmore.com

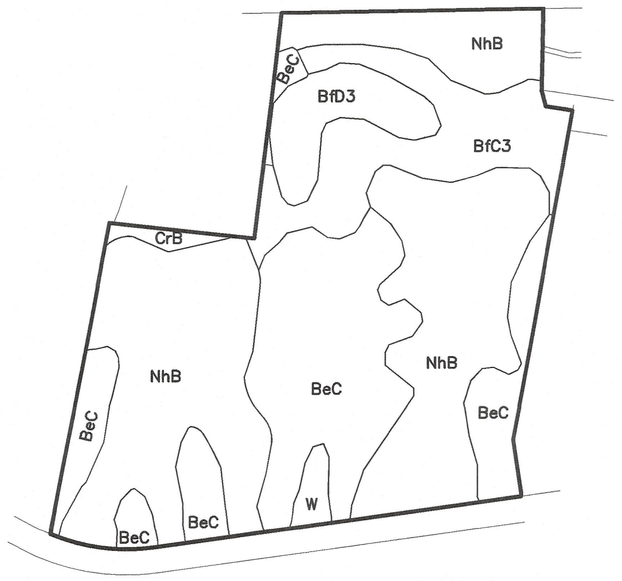


Map Unit Symbol	Map Unit Name	Acres in AOI	Percent of AOI
BeC	Beasley silt loam, 6 to 12 percent slopes	21.1	30.4%
BfC3	Beasley silty clay loam, 6 to 12 percent slopes, severely eroded	8.8	12.7%
BfD3	Beasley silty clay loam, 12 to 20 percent slopes, severely eroded	3.9	5.6%
CrB	Crider silt loam, 2 to 6 percent slopes	0.5	0.8%
NhB	Nicholson silt loam, 2 to 6 percent slopes	34.3	49.3%
W	Water	0.9	1.3%
Totals for Area of Interest		**69.6**	**100.0%**

SOILS MAP
NOT TO SCALE

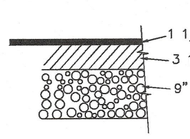


PROPOSED ROAD PAVEMENT DETAIL
NOT TO SCALE

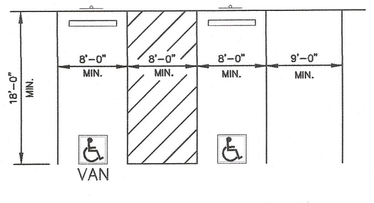


24' MINIMUM WIDTH OF AISLEWAY

TYPICAL PARKING SPACE LAYOUT
NO SCALE

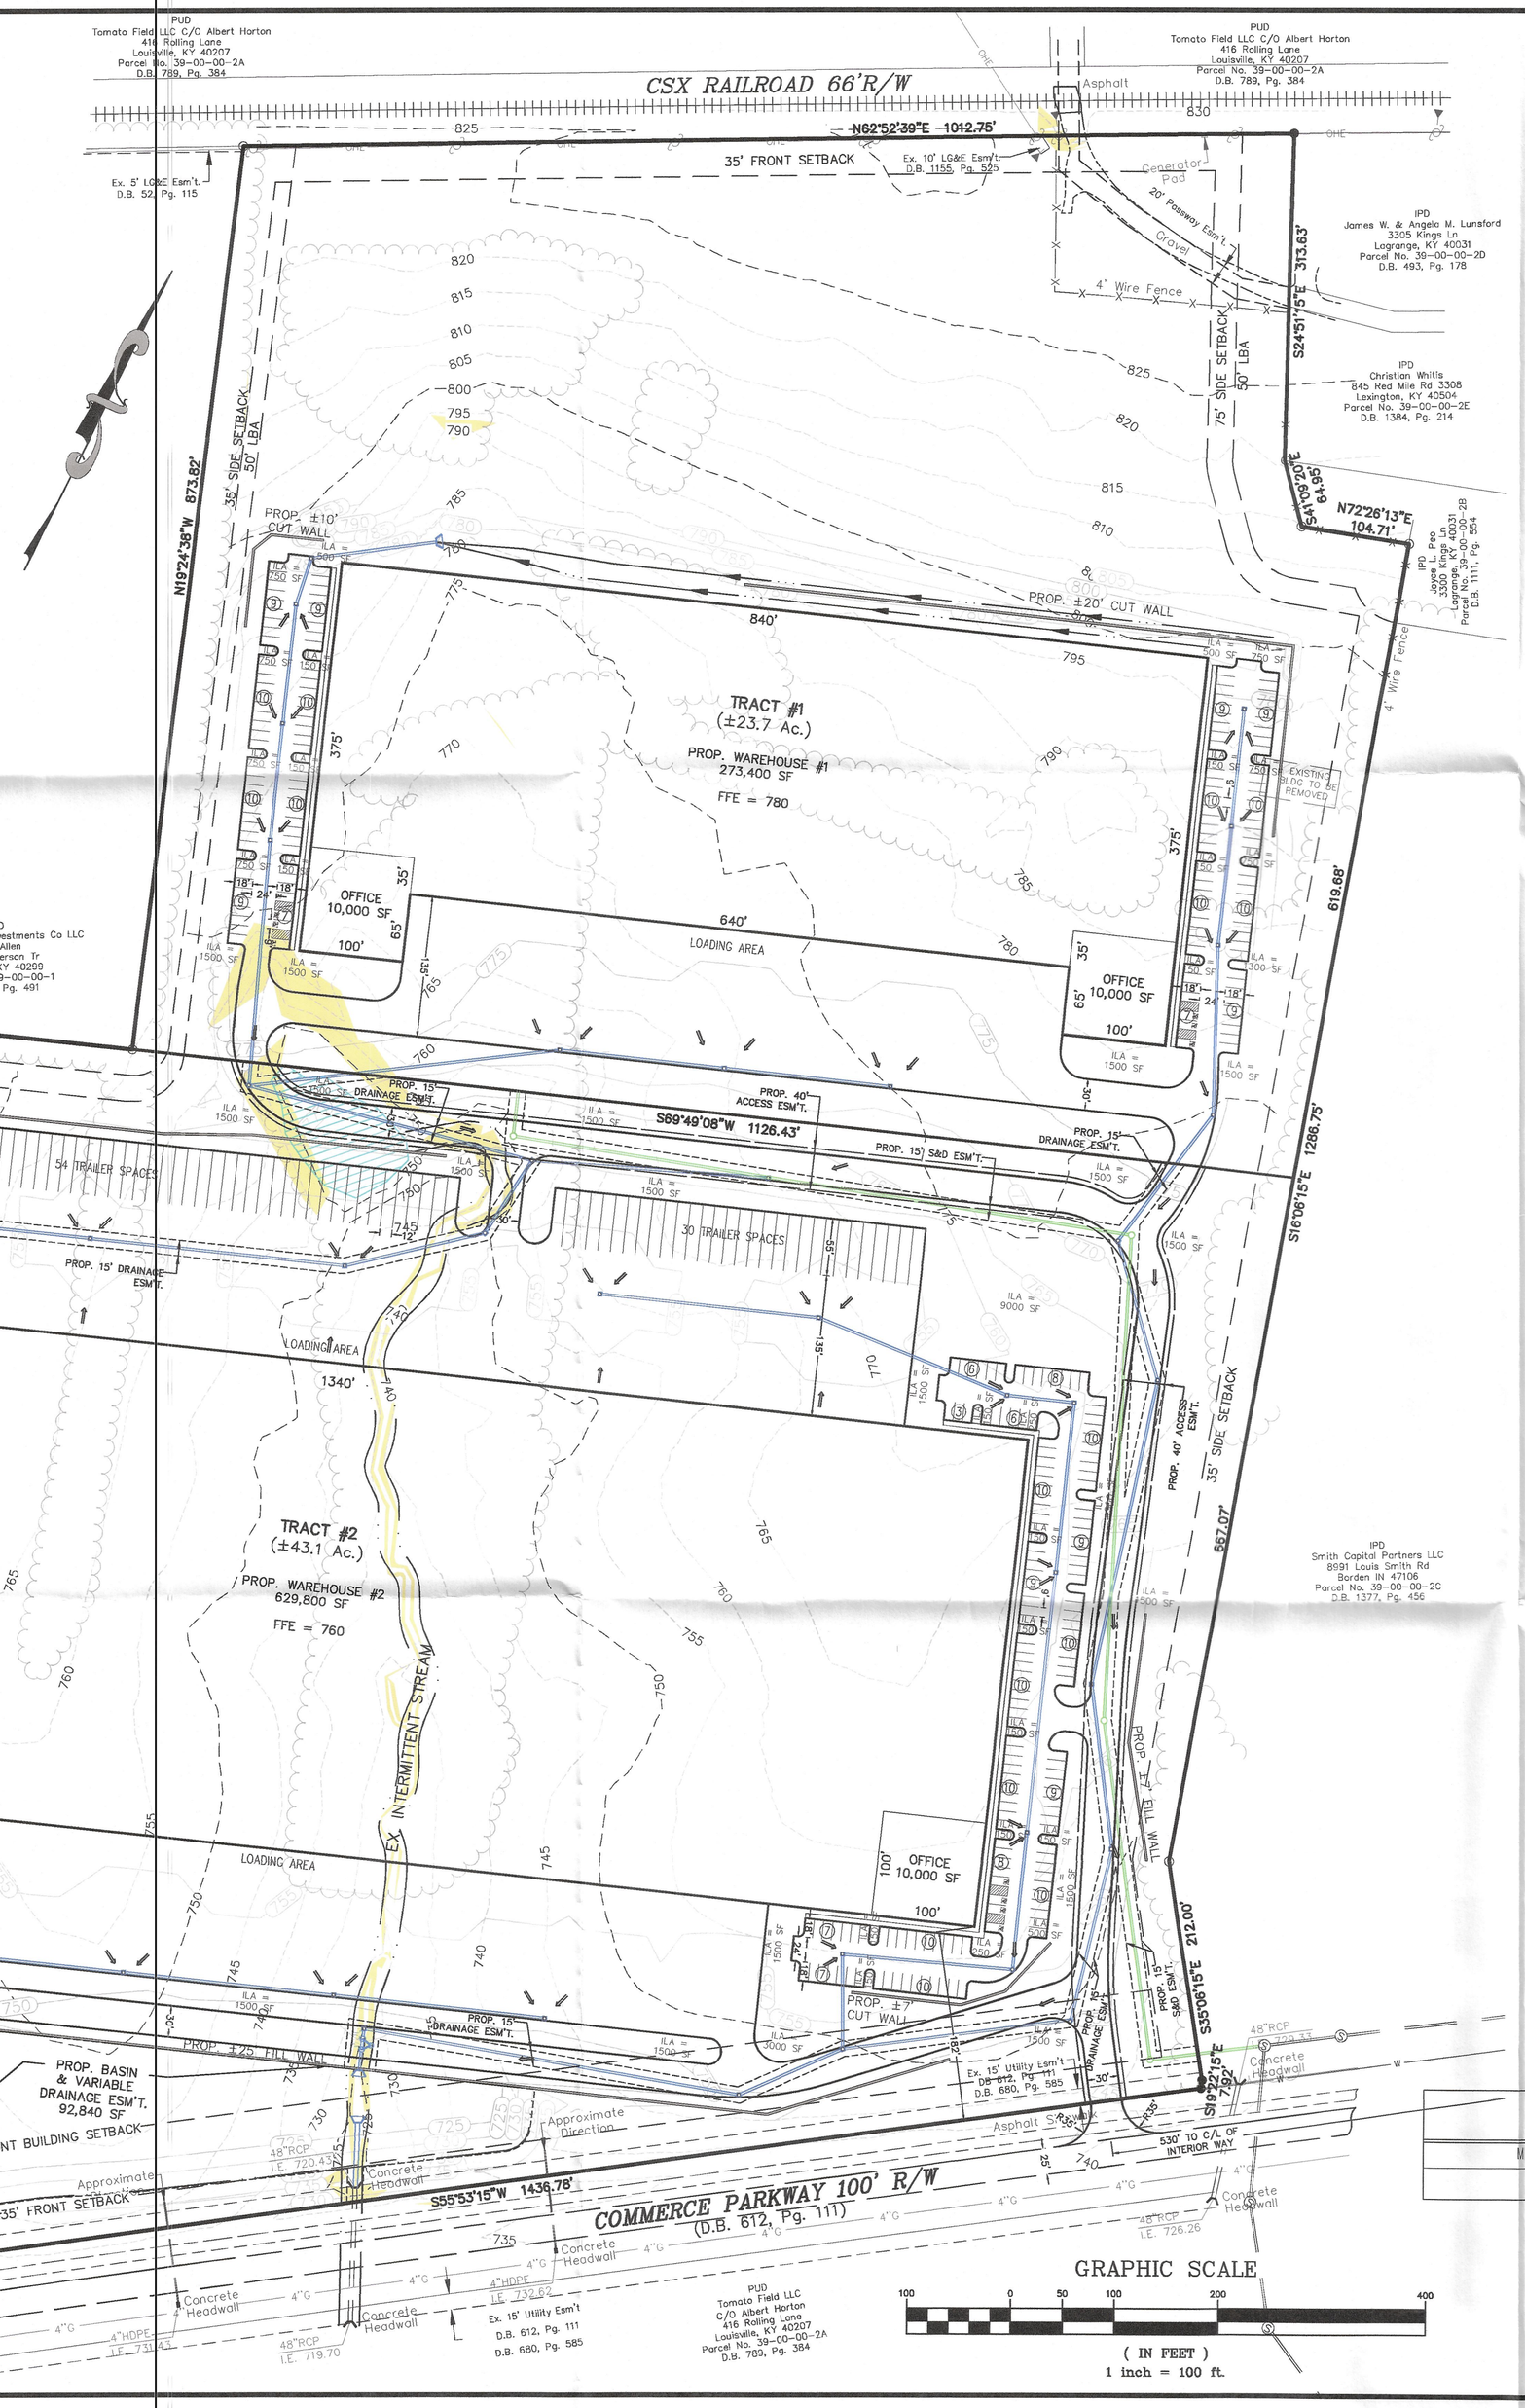

LEGEND
- = PROPOSED STORM SEWER, CATCH BASIN
- = PROPOSED SEWER AND MANHOLE
- = PROPOSED DRAINAGE SWALE
- = EXISTING STORM SEWER, CATCH BASIN
- = EXISTING SEWER AND MANHOLE
- = EXISTING CONTOUR
- = PROPOSED CONTOUR
- = PROPOSED WATER LINE
- = EXISTING JURISDICTIONAL WETLAND
- = PROPOSED WATER QUALITY UNIT

GRAPHIC SCALE
100 0 50 100 200 400
(IN FEET)
1 inch = 100 ft.

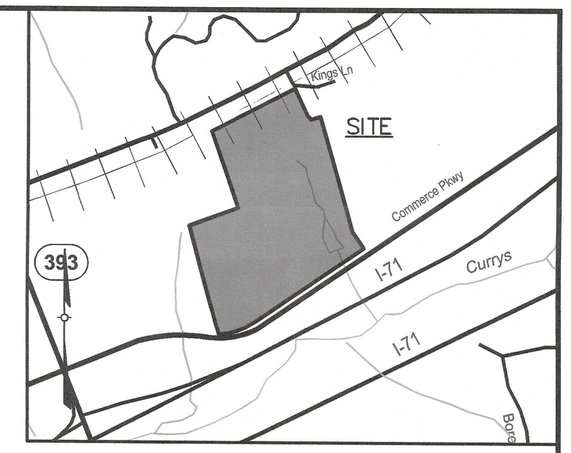

LOCATION MAP
NOT TO SCALE

PROJECT DATA

TOTAL SITE AREA	= ±66.8 Ac. (2,909,302 SF)
TRACT #1	= ±23.7 Ac. (1,032,987 SF)
TRACT #2	= ±43.1 Ac. (1,876,315 SF)
EXISTING ZONING	= PUD
PROPOSED ZONING	= I-1
EXISTING USE	= UNDEVELOPED
PROPOSED USE	= LOGISTICS WAREHOUSE

TRACT #1 DATA

BUILDING HEIGHT	= 36' (50' MAX. ALLOWED)
BUILDING AREA	= 273,400 SF
LOT COVERAGE	= 26% (75% MAX. ALLOWED)

PARKING REQUIRED	MIN.	MAX.
WAREHOUSE (100 EMPLOYEES)		
1 SP/1.5 EMPLOYEE MIN.	= 67 SP	
1 SP/EMPLOYEE MAX.	=	100 SP
OFFICE (20,000 SF)		
1 SP/300 SF	= 67 SP	
1 SP/200 SF	=	100 SP
TOTAL PARKING REQUIRED	= 134 SP	200 SP

PARKING PROVIDED = 148 SPACES (6 ADA SP INCLUDED)

TOTAL VEHICULAR USE AREA	= 144,143 SF
INTERIOR LANDSCAPE AREA REQUIRED	= 14,414 SF (10% OF VUA)
INTERIOR LANDSCAPE AREA PROVIDED	= 14,450 SF
PROPOSED IMPERVIOUS	= 417,543 SF/40% (90% MAX. ALLOWED)

TRACT #2 DATA

BUILDING HEIGHT	= 40' (50' MAX. ALLOWED)
BUILDING AREA	= 629,800 SF
LOT COVERAGE	= 34% (75% MAX. ALLOWED)

PARKING REQUIRED	MIN.	MAX.
WAREHOUSE (200 EMPLOYEES)		
1 SP/1.5 EMPLOYEE MIN.	= 133 SP	
1 SP/EMPLOYEE MAX.	=	200 SP
OFFICE (20,000 SF)		
1 SP/300 SF	= 67 SP	
1 SP/200 SF	=	100 SP
TOTAL PARKING REQUIRED	= 200 SP	300 SP

PARKING PROVIDED = 295 SPACES (8 ADA SP INCLUDED)

TOTAL VEHICULAR USE AREA	= 547,761 SF
INTERIOR LANDSCAPE AREA REQUIRED	= 54,776 SF (10% OF VUA)
INTERIOR LANDSCAPE AREA PROVIDED	= 56,250 SF
PROPOSED IMPERVIOUS	= 1,177,561 SF/63% (90% MAX. ALLOWED)

GENERAL NOTES:
1. Parking areas and drive lanes to be a hard and durable surface.
2. An encroachment permit and bond will be required for all work done in the right-of-way.
3. No portion of the site is within the 100 year flood plain per FEMA Panel 21185 C 0120 E dated October 16, 2025.
4. Drainage patterns depicted by arrows (⟹) is for conceptual purposes.
5. Pursuant to Section 6.3.C of the Oldham County Subdivision Regulations, the paved traffic areas shall be curbed.
6. Prior to the completion of construction of this development, the existing multi-use trail/sidewalk along the site frontage of Commerce Pkwy shall be maintained, removed, and/or replaced as necessary.
7. Prior to building permit approval, a landscape plan must be submitted and approved. The landscape plan shall identify any existing significant trees.

DETENTION BASIN CALCULATIONS

X = Δ CRA/12
ΔC = 0.80-0.35=0.45
A = 66.8 ACRES
R = 2.8 INCHES
X = (0.45)(66.8)(2.8)/12 = 7.014 AC.-FT
REQUIRED X = 305,530 CU.FT.

PROVIDED BASIN = 92,840 SQ.FT.

TOTAL = 92,840 SQ.FT. @ APPROX. 7 FT. DEPTH
= 649,880 CU.FT. > 305,530 CU.FT.

SLOPES TABLE

MINIMUM SLOPE	MAXIMUM SLOPE	COLOR
30.00%	>	

OWNER:
TOMATO FIELD LLC
C/O ALBERT HORTON
416 ROLLING LANE
LOUISVILLE, KY 40207

SITE ADDRESS:
HWY 146
LAGRANGE, KY 40031
PARCEL #39-00-00-2A
D.B. 789, PG. 384

REVISIONS	NO.	DATE	DESCRIPTION	BY

SURVEYOR'S SEAL

ENGINEER'S SEAL

PROJECT DATA
FILE NAME: 26006 - SITE PLAN
DATE: 08.11.26
SCALE: AS SHOWN
CHECKED BY: ZS
DRAWN BY: ZS

L D&D
LAND DESIGN & DEVELOPMENT, INC.
ENGINEERING • LAND SURVEYING • LANDSCAPE ARCHITECTURE
625 WASHBURN AVENUE, SUITE 105, LOUISVILLE, KENTUCKY 40222
PHONE: 502.412.5974
WEB SITE: WWW.LDS-KY.COM

DEVELOPMENT PLAN
WAREHOUSE COMMERCE PARKWAY
DEVELOPER
GLENVIEW PARTNERS
6363 POPLAR AVE SITE 240
MEMPHIS, TN 38119

JOB NO. 26006

SHEET 1 OF 1

G:\Current Projects\26006\DWG\Planning\26006 - SITE PLAN - 20260824.dwg, 8/27/2026 8:56:56 AM, DWG To PDF.pc3

Secretary Christy Edgar called and read Docket:

DOCKET PZ-26-024 – An application has been filed by Glenview Partners Acquisitions, LLC for a Zoning Map Amendment and Development Plan on property located at the 3000 block of Commerce Pkwy, La Grange. The property is 66.8 acres and zoned PUD, Planned Unit Development District with a proposed zoning of I-1, Light Industrial District.

1. **Introduction of the new information by staff and questions by the Commission:**

Planner Cayley Crum presented the following:

- Summary of the application.
- Case History (see Exhibit A, Staff Report dated September 22, 2026).
- Site history.
- Aerial Photos of the site.
- Photos of property.

Jim Silliman, Oldham County Engineer

- The land-disturbance will be greater than one acre so the applicant will need to obtain a KYR10 Permit from the Kentucky Division of Water and an Oldham County Stormwater Quality Management and Erosion Control permit from Oldham County Engineering Department.
- There is a blue line stream on the property, and the applicant will need to coordinate with the Army Corps of Engineers and the Division of Water for permitting.
- The storm water detention must be in accordance with our post construction runoff ordinance.
- The construction site plans must be developed to include erosion control measures in accordance with our construction site runoff ordinance.
- The traffic study does indicate a need for a left turn lane.

Commissioner Servis asked, tract one has an elevation of 780 and tract two is at 760, so will this be a terrace site?

County Engineer Silliman replied, you will need to ask the applicant.

Commissioner Douglas asked, what is required for the applicant to get KY DOW's permission to build over the blue line stream?

County Engineer Silliman replied, that will be determined by the Corp of Engineers and

Division of Water at that time.

Commissioner Douglas asked, will the 30 feet be wide enough for tractor trailers to enter at the entrance?

County Engineer Silliman replied, this is a preliminary plan, and during the construction

plan review, we will require turn radius diagrams to justify what the turn radius is.

2. **Presentation by the applicant or representative and others in support of the application:**

Cliff Ashburner, Dinsmore & Shohl, 101 S. 5th Street, Louisville, was present and representing the applicant.

- This is a proposed zoning map amendment from PUD to I-1.
- We are proposing to build spec warehouse buildings.
- The property will be somewhat terraced.
- The residence on Kings Lane is about 40 feet above the finish floor area of the northernmost building.
- Tract one is 23.7 acres and tract two is 43.1 acres.
- Single point of access from Commerce Pkwy.

Zoe Sermersheim, Land Design & Development, 503 Washburn Ave, Louisville, was present and sworn in prior to presenting.

- Tract two will provide an access easement to get to tract one.
- Tract one will have a 273,000 square foot building with parking and loading docks.
- Tract two will have a 629,000 square foot building with parking and loading docks and trailer spaces.
- We will have additional screening along the loading docks facing Commerce Parkway on tract 2.
- Kings Lane will remain open.

3. **Testimony and questions by those opposing the application: None**
4. **Questioning of the applicant and those opposing the application by the Commission:**

Commissioner Hampton asked, what's the plan for the acreage on the north from tract one?

Todd Blanton, Glen View Partners, 40 S. Main Street, Memphis, TN, was present and sworn in prior to replying, there is a huge grade change there, so it will stay unchanged.

Commissioner Servis asked, will the buildings be constructed concurrently together or the smaller one first?

Mr. Blanton replied, our plan is to build them simultaneously.

Commissioner Douglas asked, will there be rear access to tract one for the fire department to access the back of that building?

Mr. Blanton replied, no, because of the grading of that property.

Commissioner Douglas asked, is it standard for a 30-foot width for fire trucks to get in or out?

Mrs. Sermersheim replied, yes.

5. **Rebuttal evidence and Cross Examination by the Applicant: None**
6. **Rebuttal evidence and Cross Examination by the Opposition: None**
7. **Final statement of the Opposition: None**
8. **Final statement of the Applicant:**

Attorney Ashburner's final statement:

- We believe that this does meet the comprehensive plan and the comprehensive plan shows this area as mixed use.

END OF PUBLIC HEARING

Director Fischer summarized the docket.

FINDINGS AND DECISIONS
Docket PZ-26-024
Zoning Map Amendment
3000 Block of Commerce Pkwy

Motion was made by Commissioner Kraus and seconded by Commissioner Elder to recommend approval to the Oldham County Fiscal Court for a zoning map amendment from PUD to I-1 located at 3000 Block of Commerce Parkway, LaGrange, because it complies with objective LU-1 and LU-3 of the comprehensive plan and it's compatible with the existing and anticipated land use and it supports economic growth in our community due to the testimony that we received today. This motion also includes the following Binding Elements.

Binding Elements

1. The approval applies only to the plan presented at the September 22, 2026, Oldham County Planning Commission public hearing.
2. The plan must comply with all established federal, state and county ordinances and requirements and comply with all necessary easement restrictions at the time of construction plan approval.

The vote was as follows:

YES: Commissioners Allen, Allison, Davis, Douglas, Elder, Graham, Hampton, Hayes, Kraus, Miller, and Servis.

NO: None

ABSTAIN: None

ABSENT: Commissioner Klingenfus, Marsh and Thompson.

Motion approved on a vote of 11-0

FINDINGS AND DECISIONS
Docket PZ-26-024
Development Plan
3000 Block of Commerce Pkwy
LaGrange

Motion was made by Commissioner Kraus and seconded by Commissioner Davis to approve the development plan located at 3000 Block of Commerce Pkwy, LaGrange because it complies with objectives LU-1 and LU-3 of the comprehensive plan, the zoning ordinance and the subdivision regulations based on evidence and testimony heard today. This motion also includes the following Binding Elements.

Binding Elements

1. The approval applies only to the plan presented at the September 22, 2026, Oldham County Planning Commission public hearing.
2. The applicant shall obtain all necessary permits and inspections from the appropriate agencies.
3. There shall be no changes to the plan without review by the Oldham County Planning Commission and Engineer's Office.
4. The plan must comply with all established federal, state and county ordinances and requirements and comply with all necessary easement restrictions at the time of construction plan approval.
5. A landscaping and lighting plan will be required at time of construction plan submittal.

The vote was as follows:

YES: Commissioners Allen, Allison, Davis, Douglas, Elder, Graham, Hampton, Hayes, Kraus, Miller, and Servis.

NO: None

ABSTAIN: None

ABSENT: Commissioner Klingenfus, Marsh and Thompson.

Motion approved on a vote of 11-0.

Technical Review Committee Meeting
Wednesday, August 19, 2026
Meeting at 1:00 p.m.

PRESENT:

TRC Committee Members:
Ryan Fischer – Oldham County Planning & Development
Cayley Crum – Oldham County Planning & Development
Jim Silliman – Oldham County Engineer
Matt Tolar - Oldham County GIS
Brian Claybern – LaGrange Fire & Rescue Department
Russ Rose – Oldham County Water District

****

APPLICANT NAME AND ADDRESS OF PROPOSAL

TRC-26-016 Glenview Partners, HWY 146

Zoning Map Amendment and Development Plan
Current Zoning – PUD, Planned Unit District
Proposed Zoning – IPD, Industrial Park District
Applicant – Glenview Partners, Tomato Field LLC
Engineer – Land Design & Development, Inc. (LD&D)

Cliff Ashburner, Dinsmore & Shohl, 101 S. Fifth Street, Louisville

- Applicants want to rezone the property from PUD to I-1 to accommodate two buildings.

Zoe Sermersheim, Land Design & Development, 503 W. Washburn Ave., Louisville

- The property is 66.8 acres.
- Tract 1 (north) will have a 273,400 SqFt building with parking and loading docks.
- Tract 2 (south) will have a 628,800 SqFt building with parking, loading docks and trailer spaces.
- Stormwater to basin at southern middle, outfall across Commerce Parkway.
- Sanitary will be connected to existing service line.

AGENCY COMMENTS:

Cayley Crum, Planner, Oldham County Planning and Development Services

1. Indicate the areas of substantial trees including a general description of their type and sizes.
2. Indicate lakes, ponds, marshes, wetlands, and soil types.
3. Note whether there are any areas of steep slope (over 30%).
4. Indicate the provisions for screening, buffering, and landscaping.
5. Indicate proposed building height.
6. Indicate 20,000 SF Office location in tract 2 drawings or adjust parking to 100 spaces less.
7. Clarify office versus warehouse space on drawing, then recalculate lot area coverage if applicable.
8. Clarify where truck loading area will occur on drawing.
9. Recalculate square foot calculation from acreage under Project Data.

Cayley Crum read KYTC, Jason Richardson's comments.

- This does not directly connect to a state highway.
- The development is of sufficient size to warrant a traffic impact study analyzing the impacts from the development's traffic on Commerce Parkway at the intersections with the state highways in each direction.

Cayley Crum read LG&E / KU, Delana Gideons' comments.

- There is a 3ph electric on the south side of LaGrange and the north side of their property.
- Electric stops on Commerce Parkway & Interior, the applicant will need an extension if they want it fed from the south side of their property.

Cayley Crum read USPS, Stephanie VanZante's comments.

- Since there are two tracts they will need separate mailboxes.

Matt Tolar, Oldham County GIS

- Just get with me for the addresses.

Jim Silliman, Oldham County Engineer

1. Permits:

a. Because land-disturbing area will be greater than one (1) acre, the applicant shall obtain a KYR10 Permit from the Kentucky Division of Water (KY DOW) and a Stormwater Quality Management and Erosion Control (SWQMEC) Permit from Oldham County.

b. Based on an assessment using the USGS The National Map, the project involves land-disturbance within and/or along jurisdictional waters/wetlands. As such, the applicant shall provide appropriate permits from both the USACE and KYDOW. Permits may include a 404 Permit, 401 WQC Permit, and Permit for Construction In or Along a Stream. If in-stream detention is also planned, individual permitting from those agencies may also be required.

2. Road/Pavement/Sidewalk Design:

a. 1) The 2025 Commerce Parkway Traffic Study indicates 3 potential access points. The proposed plan reduces that to one entrance.

2) That proposed entrance is approximately 440' west of Interior Way. The Commerce Parkway Traffic Study proposes a spacing of 720' from Interior Way. It appears the single proposed entrance may be realigned approximately 90' to the west increasing the spacing from Interior Way to approximately 530'. This can be done by maintaining the street intersection standards within the Oldham County Subdivision Regulations that require the road be at a 90 degree angle a distance of at least 50' from the intersecting road.

3) For further reference, Commerce Parkway is currently indicated as a Major Urban Collector Street within Kentuckiana Regional Planning and Development Agency (KIPDA) mapping. Based on Section 320-030 of the Oldham County Comprehensive Zoning Ordinance, the driveway spacing shall be at least 300 feet and spacing between major intersections between 300' and 600'.

4) Considering this information, I recommend the intersection of the proposed entrance with Commerce Parkway be shifted approximately 90' to the west as noted above.

b. We recommend the applicant design the planned entrance encroaching onto Commerce Parkway to comply with the KYTC D5 Standard Commercial Entrance detail.

c. Pavement cross section was not provided with the plan. This shall be provided on the plan submitted for the Planning Commission hearing.
d. Pursuant to Section 6.3.C of the Oldham County Subdivision Regulations, the paved traffic areas shall be curbed.
e. Considering the planned use, we assume the internal streets, driveways, and common parking areas will be private (e.g., not be dedicated to public use) and shall be maintained by the owners.
f. The applicant shall ensure the internal pavement geometry can accommodate potential vehicles using the pavement (e.g., emergency vehicles, garbage trucks, delivery trucks, etc.). This shall be shown through turning movement diagrams during the construction plan review process.
g. The existing multi-use trails (sidewalks) shall be maintained, or removed and replaced, as part of this project.
h. Details for any area requiring a retaining wall and fall protection shall be provided with the SWQMEC permit application

3. Stormwater Runoff and Water Quality:
a. Since the land-disturbance area is equal-to or greater-than one (1) acre, stormwater detention or retention and water quality treatment will be required per Oldham County Ordinance No. 16-830-348. The applicant will be required to provide these calculations with their SWQMEC permit application.
b. Water quality treatment will be required per Sections 5.3 and 6.0 of the Oldham County Ordinance Post-Construction Stormwater Control Ordinance
c. New detention/retention basins shall have the following attributes:
1) No trees will be permitted within the 100-year WSE of the basin.
2) The outlet headwall of the detention basin should be set-back 15-ft from the property line.
3) The emergency spillway shall not be earthen. It shall incorporate an appropriate channel lining.
d. The detention/retention basins shall be encompassed by a drainage easement, which shall be recorded with the Oldham County clerk with an associated Long-Term Stormwater Maintenance Agreement. Please note, the release of erosion control surety may be delayed until this easement has been recorded with the county clerk.
e. To ensure this project remains compliant with typical construction phasing and sequencing, Oldham County Engineering will require the detention basins be built first and act as sediment basins for the duration of the project. Oldham County Engineering will not permit building foundations/pads, roadways, or any other hardscapes to be constructed prior to the completion of the sediment basins. This requirement shall be clearly outlined in the construction plan's Phasing and Sequencing notes.

4. Traffic Impact: Based on the gross floor area of the proposed buildings, the Institute of Transportation Engineers (ITE) web-based trip generation tool calculates between 108 and 154 peak hour trips. Review of the KYTC interactive traffic map online indicates an ADT of 6068 in 2025 (Station B33) on Commerce Parkway near the project location. In accordance with the Oldham County Subdivision Regulations, a Traffic Impact Study (TIS) is required.

Brian Claybern, LaGrange Fire & Rescue Department
- Show FDC locations; ensure within 100 feet of hydrants.
- Hydrants no more than 300 feet spacing around the property.
- Consider rear access for tract 1 building.

Russ Rose, Oldham County Water

- There is currently no water in front of this property so it will require an extension.

Public Comments: None

****

Neighborhood Meeting Notes

Hwy 146, Oldham County, KY

The meeting was held on July 16, 2026, at the John W. Black Community Center. The applicant, Glenview Partners, was represented by Todd Blanton; Cliff Ashburner of Dinsmore & Shohl LLP; and Zoe Semersheim of Land Design & Development.

Mr. Ashburner provided an overview of the application process and outlined the upcoming public hearing and meeting schedule. Ms. Semersheim presented the proposed site plan, including the layout of the development and stormwater drainage improvements. Mr. Blanton discussed the suitability of the location, noting that the site is not closely situated to residential properties and is not located in a high-traffic area. He also highlighted Glenview Partners' history of successful developments in Oldham County and expressed the company's desire to continue its partnership and investment in the community.

The application requests the rezoning of the property from Planned Unit Development (PUD) to Industrial Park District (IPD) to facilitate the construction of two logistics warehouse facilities.

Following the presentation, the neighboring property owners and residents in attendance did not have any additional questions or comments for the applicant's representatives.

The meeting concluded after approximately 30 minutes.

MEETING SIGN IN SHEET

Property: Highway 146 – Oldham County
Zoning From PUD Planned Unit Development to IPD Industrial Park District
Neighborhood Meeting: July 16, 2026

NAME (Please print)	ADDRESS	EMAIL
Joyce Reed	3300 Kings Ln. LaGrange	
Alex Tarvel	2201 Interior way	ATarvel@PUTEngineers.com
Larry Otterback	4009 Briar Ridge Rd.	LarryOtterback@icloud.com
Rob Houchens	11100 Yager Lane	RobforJudgeExec@gmail.com